TRUNG TÂM DẠY NGHỀ LÁI XE HIỆP PHÁT

ĐỊA ĐIỂM XD: XÃ TÂN NHỰT - HUYỆN BÌNH CHÁNH - THÀNH PHỐ HỒ CHÍ MINH

CHỦ ĐẦU TƯ: CÔNG TY TNHH Ô TÔ HIỆP PHÁT

ĐỊA CHỈ: 276 - ĐƯỜNG MINH PHỤNG - PHƯỜNG 2 - QUẬN 11 - TP. HCM

BẢN ĐỒ TỔ CHỨC KHÔNG GIAN KIẾN TRÚC CẢNH QUAN (MỞ RỘNG) (TL: 1/500)

BẢNG THÔNG SỐ KỸ THUẬT XE (SÂN SÁT HẠCH ĐÃ THI CÔNG):

I. Thông số kỹ thuật xe sát hạch

TT	Tên gọi	Ký hiệu	Hạng xe			
			B VIOS 1.5E(2017)	C THACO OLLIN450A - XTL	D COUTY HD2F/E3	E TRANSINCO (BA-HAI CA K52 E2)
1	Chiều dài xe	a	4410,00	7630,00	7060,00	10500,00
2	Chiều rộng xe	b	1700,00	2240,00	2080,00	2500,00
3	Chiều rộng bánh xe sau	B1	185,00	500,10	440,00	500,00
4	Bán kính quay vòng nhỏ nhất	Rqv	5100,00	8300,00	7400,00	10000,00
5	Chiều dài cơ sở	L	2550,00	4200,00	4085,00	5170,00

II. Kích thước hình sát hạch

TT	Hình thi	Tên gọi	Ký hiệu	Hạng xe			
				B	C	D	E
1	Vệt bánh xe	Chiều rộng vệt bánh xe	Bvb	385,00	700,10	640,00	790,00
		Chiều dài vệt bánh xe	Lvb	4410,00	7630,00	7060,00	10500,00
2	Đường vuông góc	Chiều sâu đường vuông	Sv	6615,00	11445,00	10590,00	15750,00
		Chiều dài đường vuông	Lv	8820,00	15260,00	14120,00	21000,00
		Chiều rộng đường vuông	Bv	3740,00	4928,00	4576,00	5500,00
3	Đường vòng quanh co	Bán kính quay vòng ngoài	Rn	6300,00	9500,00	8600,00	11200,00
		Chiều rộng đường quanh co	Bqc	3740,00	4928,00	4576,00	5500,00
		Bán kính quay vòng trong	Rtr	2560,00	4572,00	4024,00	5700,00
		Khoảng cách tâm 2 phía	Sqc	8860,00	14072,00	12624,00	16900,00
4	Ghép xe ngang	Chiều dài nơi đỗ	Lg	6615,00		11766,67	17500,00
		Chiều rộng nơi đỗ	Rg	2125,00		2600,00	3125,00
5	Ghép xe dọc	Chiều dài nơi ghép	Ld	5410,00	8630,00		
		Chiều rộng nơi ghép	Rd	2300,00	2840,00		
		Khoảng cách không chế	Ed	5292,00	9156,00		

QUY TRÌNH SÂN ĐÀO TẠO LÁI XE Ô TÔ HẠNG B, C (MỞ RỘNG):

1. - XUẤT PHÁT
2. - DỪNG XE TẠI ĐƯỜNG DÀNH RIÊNG CHO NGƯỜI ĐI BỘ
3. - DỪNG VÀ KHỞI HÀNH XE NGANG DỐC
4. - VÀO HÌNH VỆT BÁNH XE ĐƯỜNG HẸP VUÔNG GÓC
5. - ĐI THẲNG QUA NGÃ TƯ CÓ TÍN HIỆU ĐIỀU KHIỂN GIAO THÔNG
6. - VÀO HÌNH ĐƯỜNG QUANH CO
7. - ĐI THẲNG QUA NGÃ TƯ CÓ TÍN HIỆU ĐIỀU KHIỂN GIAO THÔNG
8. - GHÉP XE DỌC VÀO NƠI ĐỖ ĐỐI VỚI XE HẠNG B, C
9. - RẼ TRÁI QUA NGÃ TƯ CÓ TÍN HIỆU ĐIỀU KHIỂN GIAO THÔNG
10. - DỪNG Ở CHỖ CÓ ĐƯỜNG SẮT CHẠY QUA
11. - VÀO ĐƯỜNG THAY ĐỔI SỐ TRÊN ĐƯỜNG THẲNG
12. - GHÉP XE NGANG VÀO NƠI ĐỖ ĐỐI VỚI XE HẠNG B
13. - RẼ PHẢI QUA NGÃ TƯ CÓ TÍN HIỆU ĐIỀU KHIỂN GIAO THÔNG
14. - ĐIỀU KHIỂN XE QUA VẠCH KẾT THÚC

QUY TRÌNH THI SÁT HẠCH LÁI XE Ô TÔ HẠNG B, C, D, E (ĐÃ THI CÔNG):

1A. - XUẤT PHÁT
2A. - DỪNG XE TẠI ĐƯỜNG DÀNH RIÊNG CHO NGƯỜI ĐI BỘ
3A. - DỪNG VÀ KHỞI HÀNH XE NGANG DỐC
4A. - VÀO HÌNH VỆT BÁNH XE ĐƯỜNG HẸP VUÔNG GÓC
5A. - ĐI THẲNG QUA NGÃ TƯ CÓ TÍN HIỆU ĐIỀU KHIỂN GIAO THÔNG
6A. - VÀO HÌNH ĐƯỜNG QUANH CO
7A. - ĐI THẲNG QUA NGÃ TƯ CÓ TÍN HIỆU ĐIỀU KHIỂN GIAO THÔNG
8A. - GHÉP XE DỌC VÀO NƠI ĐỖ ĐỐI VỚI XE HẠNG B, C
9A. - GHÉP XE NGANG VÀO NƠI ĐỖ ĐỐI VỚI XE HẠNG D, E
10A. - RẼ TRÁI QUA NGÃ TƯ CÓ TÍN HIỆU ĐIỀU KHIỂN GIAO THÔNG
11A. - DỪNG Ở CHỖ CÓ ĐƯỜNG SẮT CHẠY QUA
12A. - VÀO ĐƯỜNG THAY ĐỔI SỐ TRÊN ĐƯỜNG THẲNG
13A. - GHÉP XE NGANG VÀO NƠI ĐỖ ĐỐI VỚI XE HẠNG B
14A. - RẼ PHẢI QUA NGÃ TƯ CÓ TÍN HIỆU ĐIỀU KHIỂN GIAO THÔNG
15A. - ĐIỀU KHIỂN XE QUA VẠCH KẾT THÚC

GHI CHÚ XE SỬ DỤNG TRONG SÂN SÁT HẠCH:

- HẠNG B: SỬ DỤNG XE VIOS 2017 1.5E
- HẠNG C: SỬ DỤNG XE THACO OLLIN450A - XTL
- HẠNG D: SỬ DỤNG XE COUTY HD29 E3
- HẠNG E: TRANSINCO (BA-HAI CA K52 E2)
- HẠNG Fc: SỬ DỤNG XE Ô TÔ ĐẦU KÉO SƠ MI RƠ MOÓC LOẠI 20 FEET KT(DXR)=(10.2X2.5)M


GHI CHÚ XE SỬ DỤNG TRONG ĐÀO TẠO LÁI XE Ô TÔ HẠNG B, C (MỞ RỘNG):

- HẠNG B: SỬ DỤNG XE CHEVROLET AVEO
- HẠNG C: SỬ DỤNG XE THACO OLLIN450A - XTL

GHI CHÚ:

- KÍCH THƯỚC TRONG BẢN VẼ THỂ HIỆN M.

STT	GHI CHÚ	KÝ HIỆU	TẦNG TRỆT	TẦNG LẦU 1	TẦNG LẦU 2	DIỆN TÍCH	GHI CHÚ
1	- NHÀ TUYỂN SINH, NHÀ VĂN PHÒNG KÍCH THƯỚC (6.5*14)M	M²	91.00	91.00	91.00	273.00	B
	Tầng trệt						
	- Phòng tuyển sinh	M²	60.00				
	- Phòng kế toán	M²	31.00				
	Tầng Lầu I						
	- Phòng GĐ đào tạo	M²		25.00			
	- Phòng Hội đồng quản trị	M²		25.00			
	- Phòng họp	M²		41.00			
	Tầng Lầu II						
	- Phòng hội trường	M²			91.00		
2	- NHÀ HỌC LÝ THUYẾT, CĂNTIN KÍCH THƯỚC (10*40)M	M²	400.00	400.00		800.00	G
	Tầng trệt						
	- Cà phê căn tin	M²	300.00				
	- Bếp	M²	100.00				
	Tầng Lầu I						
	- Phòng máy lý thuyết	M²		50.00			
	- Phòng kiểm duyệt lý thuyết	M²		50.00			
	- Phòng ghép học sinh	M²		300.00			
3	- NHÀ VỆ SINH CHUNG	M²	55.00			45.00	H
	- Phòng vệ sinh Nữ	M²	20.00				
	- Phòng vệ sinh Nam	M²	35.00				
4	- NHÀ KHÁO THÍ THI A1, A2 KÍCH THƯỚC (5*10)M	M²	50.00			50.00	I
	- Phòng giám khảo	M²	10.00				
	- Phòng chờ thi	M²	40.00				

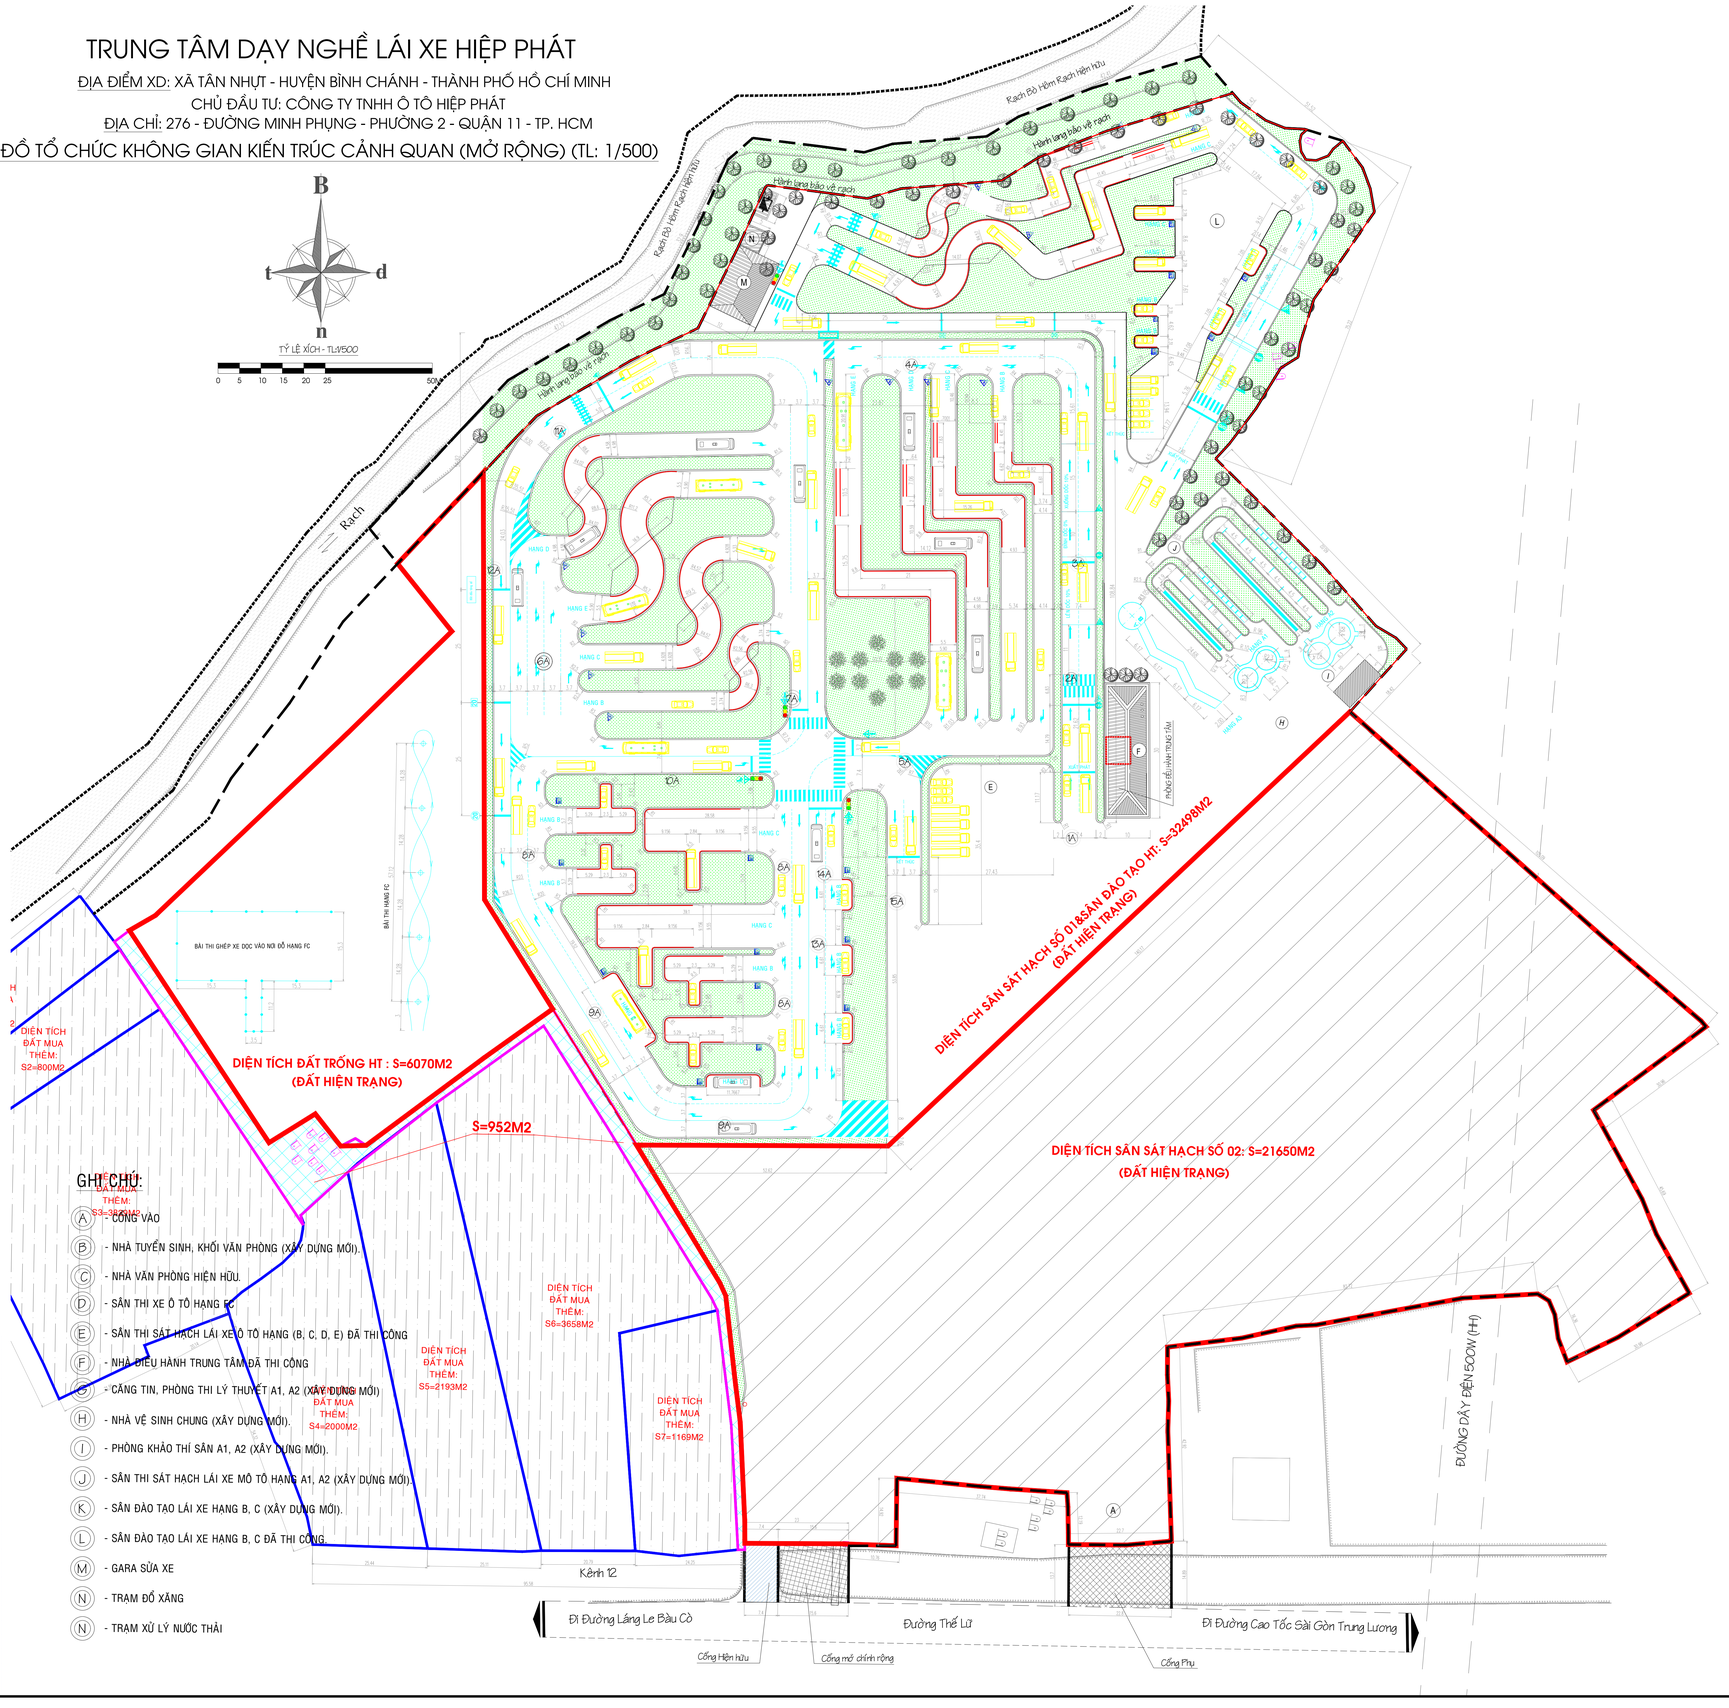

GHI CHÚ:

- A - CỔNG VÀO
- B - NHÀ TUYỂN SINH, KHỐI VĂN PHÒNG (XÂY DỰNG MỚI).
- C - NHÀ VĂN PHÒNG HIỆN HỮU.
- D - SÂN THI XE Ô TÔ HẠNG FC.
- E - SÂN THI SÁT HẠCH LÁI XE Ô TÔ HẠNG (B, C, D, E) ĐÃ THI CÔNG
- F - NHÀ ĐIỀU HÀNH TRUNG TÂM ĐÃ THI CÔNG
- G - CĂNG TIN, PHÒNG THI LÝ THUYẾT A1, A2 (XÂY DỰNG MỚI)
- H - NHÀ VỆ SINH CHUNG (XÂY DỰNG MỚI).
- I - PHÒNG KHÁO THÍ SÂN A1, A2 (XÂY DỰNG MỚI).
- J - SÂN THI SÁT HẠCH LÁI XE MÔ TÔ HẠNG A1, A2 (XÂY DỰNG MỚI).
- K - SÂN ĐÀO TẠO LÁI XE HẠNG B, C (XÂY DỰNG MỚI).
- L - SÂN ĐÀO TẠO LÁI XE HẠNG B, C ĐÃ THI CÔNG.
- M - GARA SỬA XE
- N - TRẠM ĐỔ XĂNG
- N - TRẠM XỬ LÝ NƯỚC THẢI

CHỈNH SỬA:

CHỦ ĐẦU TƯ:
CÔNG TY TNHH Ô TÔ HIỆP PHÁT

CTY. TN HỮU HẠN TƯ VẤN THIẾT KẾ XD HƯNG THỊNH

Add: 423/E Phạm Văn Chiêu - Phường 12 - Quận Gò Vấp - Tp.HCM
Tel: (08) 62559392 - Fax. (08) 62568239

GIÁM ĐỐC: NGUYỄN PHI HÙNG
CHỦ TRÌ KT: KTS. PHẠM THANH TÙ
THIẾT KẾ: KS. NGUYỄN VĂN BẠO
VẼ: HUỲNH PHẠM LÊ HUY
G.K.T: KS. NGUYỄN VĂN BẠO

TÊN CÔNG TRÌNH:
TRUNG TÂM DẠY NGHỀ LÁI XE HIỆP PHÁT
XÃ TÂN NHỰT - HUYỆN BÌNH CHÁNH - TP. HỒ CHÍ MINH

HẠNG MỤC: SÂN ĐÀO TẠO VÀ SÁT HẠCH LÁI XE (MỞ RỘNG)

NỘI DUNG BẢN VẼ: BẢN ĐỒ TỔ CHỨC KHÔNG GIAN KIẾN TRÚC CẢNH QUAN

NGÀY: .11/2018 KÝ HIỆU BV:
TK.BV.QH | BVQH: 01/01